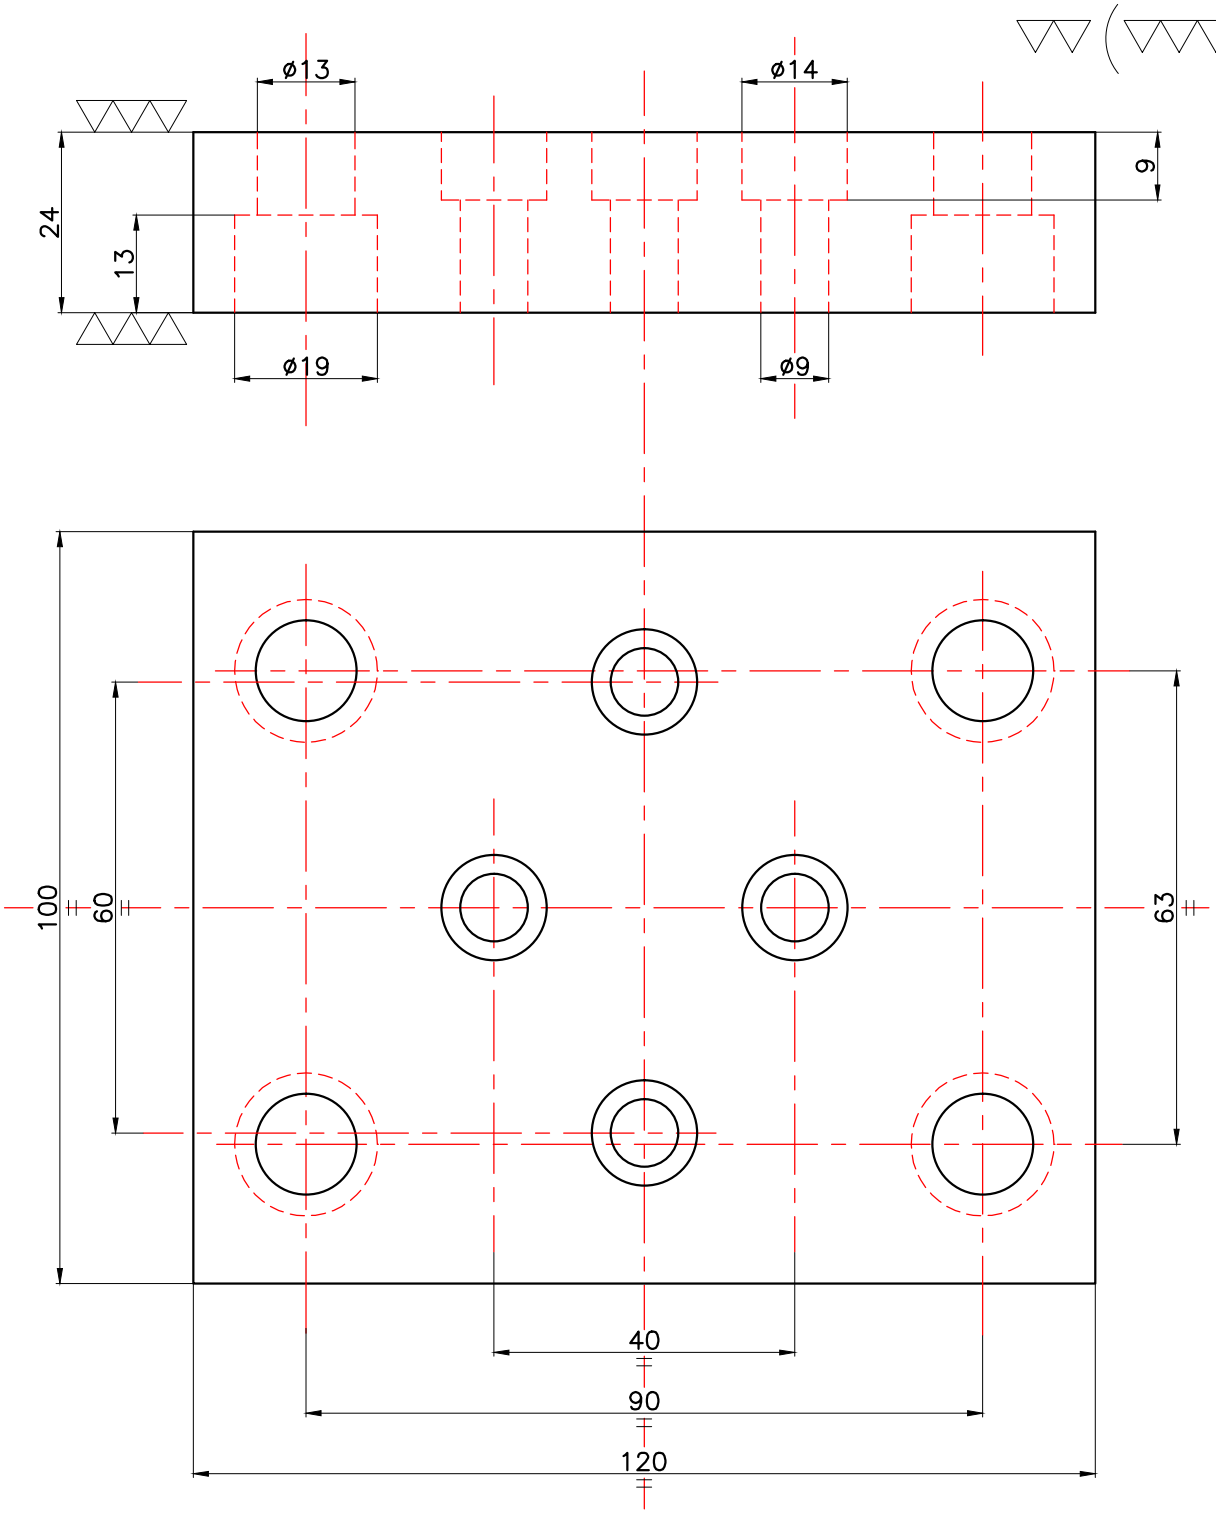

SOLO MODIFICAR EN CAD

COOPERSOL

Tomas Flores 2250 (ex Pasco)
Quilmes Oeste, BsAs Argrntina
Tel (54)(011) 4270-9731/9391
Tel (54)(011) 4270-9597

Esta prohibida la modificación, reproducción o copia total o parcial de este plano, sin la expresa autorización de la empresa COOPERSOL

MAT.: CU-EL 25 x 102 x 125

TRAT.:

CANT.: 1

Eliminar rebabas y cantos vivos salvo indicación contraria

Tolerancias no indicadas basta segun DIN 7168

ESC.: 1:1

Metodo ISO

FECHA: 12/09/16

DISP P/ SOLDAR CUPLA A TAPA TERMOTANQUE

PLACA SUPERIOR

CODIGO

CPS-9101